

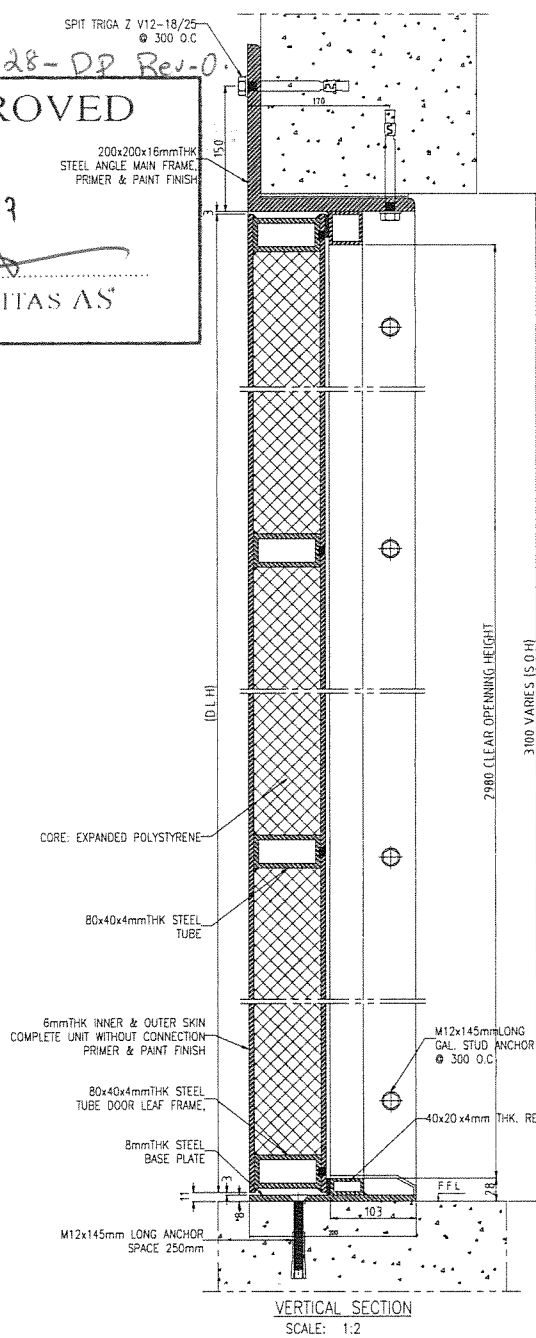
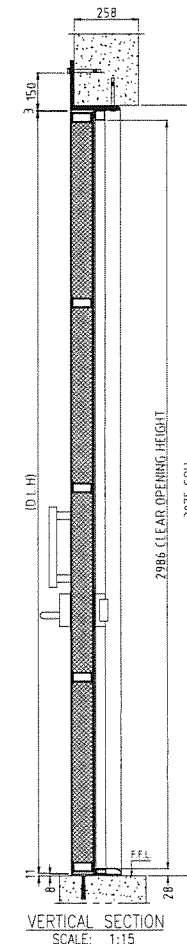
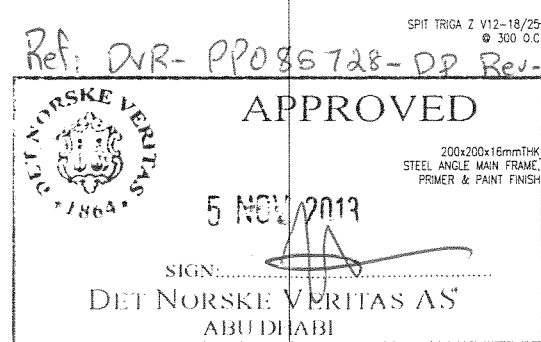


DESCRIPTION	SSW	COMPLY
FRAME	200x200x16mmTHK STEEL ANGLE	YES
LEAF SUB-FRAME	80x40x4THK STEEL SQ. TUBE	YES
LEAF	6mmTHK, INNER & OUTER SKIN AS PER CALCULATION	YES
INFILL	CORE: EXPANDED POLYSTYRENE	YES
BLAST RATING	3psi	YES
FINISH	PRIMER AND FINAL PAINT	YES


HARDWARE						
Sr. NO.	ITEM CODE	SUPPLIER	DESCRIPTION	FINISH	QTY	IMAGE
1	HINGE	CUSTOM MADE	HEAVY DUTY BARREL HINGE		8	
2	DOOR CLOSER	CALROYAL OR EQUIVALENT	OVER HEAD DOOR CLOSER	SILVER	1	
3	TOWER BOLT	CUSTOM MADE	20# TOWER BOLT	MILD STEEL	1	
4	DROP BOLT	CUSTOM MADE	20# DROP BOLT	MILD STEEL	1	
5	ADHESIVE WEATHER STRIP	KNC OR EQUIVALENT	NEOPRENE STRIP 5216	BLACK	CONTINUOUS ON REBATE	
6	PANIC DEVICE	TSB000	WITH EXT. TRIM		1	
7	WEATHER STRIP ON ALU. PROFILE	KNC OR EQUIVALENT	W-13	BLACK	CONTINUOUS ON SOFFIT	
8	THRESHOLD	CUSTOM MADE	8mmTHK STEEL FLAT	MILD STEEL	BOTTOM	
9	ANCHOR BOLT	SPIT TRIGA Z OR EQUIVALENT	TRIGA Z V12-18/25	-	20 Nos. (ON SHEAR)	
10	ANCHOR BOLT	SPIT TRIGA Z OR EQUIVALENT	TRIGA Z V12-18/25	-	10 Nos. (ON FACE)	
11	PUSH PULL HANDLE	CUSTOM MADE	HEAVY DUTY	MILD STEEL	2	
12	DOOR STOPPER	-	HEAVY DUTY	MILD STEEL		
13	STEEL ASTRAGAL	CUSTOM MADE	HEAVY DUTY	MILD STEEL	1	
14	BOTTOM SWEEP	KNC OR EQUIVALENT	W-24S OR EQUIVALENT		2	

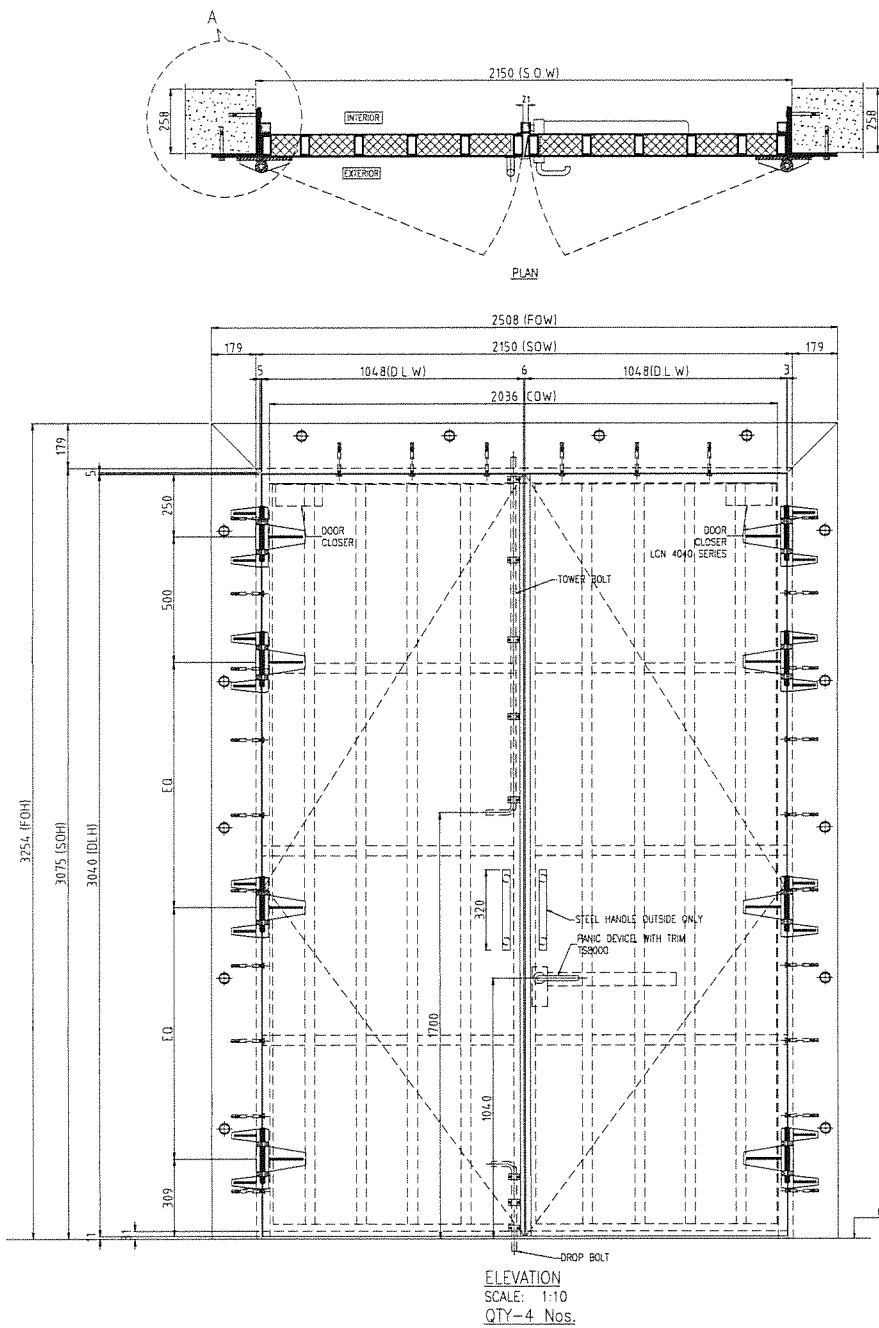


- NOTES:**
1. ALL DIMENSIONS ARE IN MILLIMETERS.
 2. ALL DIMENSIONS ON THIS DRAWING ARE SUBJECT FOR SITE VERIFICATION.
 3. ALL CONSTRUCTION & FABRICATION DETAILS ARE AS PER SSW STANDARD.
 4. SSW RESERVES THE RIGHT TO MODIFY FIXING, WELDING CONNECTION, JOINTS LOCATION & CASE THAT FABRICATION/ INSTALLATION CONSTRAINT ARISE, WITHOUT PRIOR NOTICE.
- IN STRICT CONFIDENCE:**
- BLAST PRESSURE SPECIFICATIONS:**
1. PEAK OVER $500/2500$ MILES.
 2. REFLECTED PRESSURE 50N
 3. ALL STEEL THICKS AND SHEET COMPLY WITH ASTM A53 OR EQUIVALENT
 4. ALL STEEL SHEET COMPLY WITH ASTM A 832 OR EQUIVALENT
 5. WELDING IS CONTINUOUS JOINT COMPLY WITH AWS D1.1
 6. WELDING RIG IS COMPLY WITH E 6011
 7. PAUL WELDING IS COMPLY WITH IS 5050
 8. SURFACE TREATMENT AS (NORSK STANDARD) SSPC-SP-10
 9. PRIMER COAT IS PEN-GLAZO JOTUN TYPE 200 MMS
 10. INSULATION COAT IS EXPANDED POLYSTYRENE
 11. STEEL AND/OR SPIRIT OR EQUIVALENT
 12. CUSTOM MADE STEEL PUSH-PULL HANDLE
 13. ADVANCE RUBBER SEAL STRIPS ALL AROUND ON DOOR TOPPER
 14. STEEL TENSILE BOLT FOR IN-ACTIVE LEAF
 15. STEEL DROP BOLT OR IN-ACTIVE LEAF 20mm BAR CUSTOM MADE
 16. STEEL HEAVY DUTY BARRIER, HEAVY CUSTOM MADE WITH HIGH GRADE STEEL BOLT TYPE
 17. KEY LOCK ON ACTIVE LEAF AS PER HARDWARE STD
 18. HEAVY DUTY DOOR CLOSER
 19. THRESHOLD CUSTOM MADE EQUIVALENT
 20. DRAIN DOP (BY OTHERS)
 21. STEEL AERIALGUN CUSTOM MADE /REMOVABLE

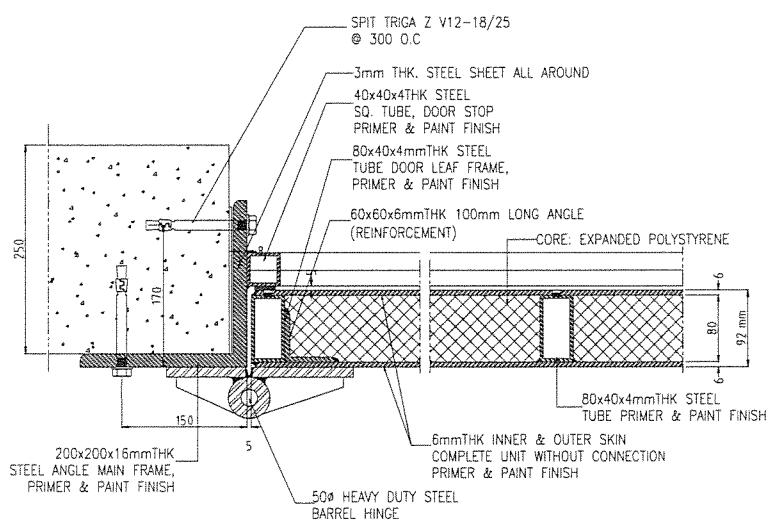


DETAIL-A
SCALE: 1:3

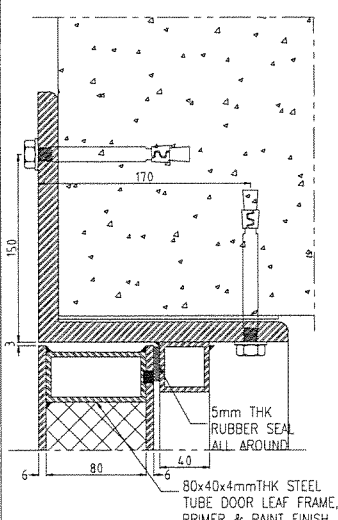


DOORS ARE AIR TIGHT
BECAUSE OF WEATHER STRIPPING

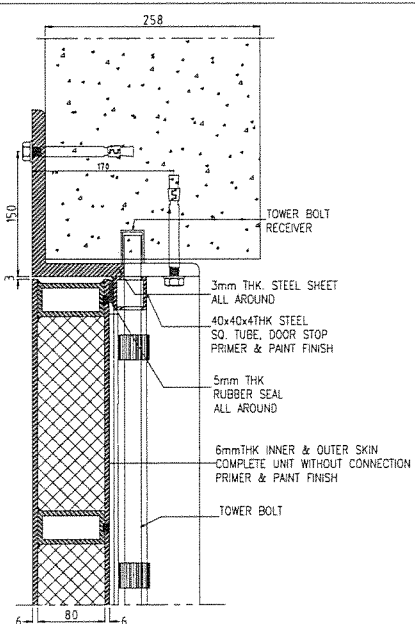

TOP FIXING DETAILS
SCALE: 1:3

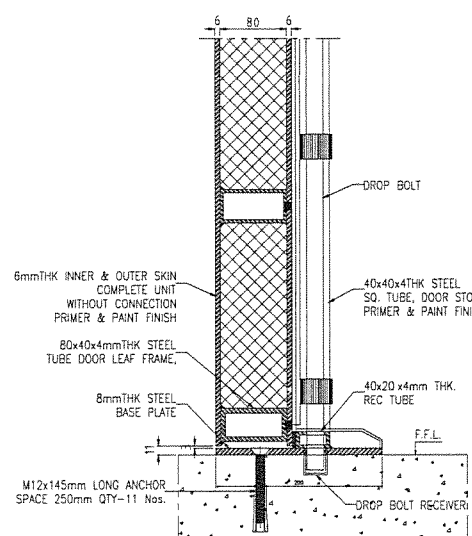

BOTTOM FIXING DETAILS
SCALE: 1:2

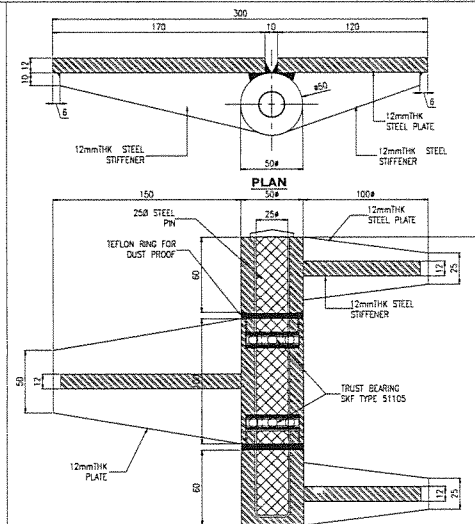

DETAIL @ WELDED STEEL BARREL HINGE
SCALE: 1:2

DOOR HANDINGS:

RRH (RIGHT HAND REVERSE ACTIVE)

RRHL (RIGHT HAND REVERSE ACTIVE LEFT)

LEGEND :

- | | |
|-----|----------------------------|
| SOW | -STRUCTURAL OPENING WIDTH |
| SOH | -STRUCTURAL OPENING HEIGHT |
| FW | -FRAME OVERALL WIDTH |
| FH | -FRAME OVERALL HEIGHT |
| DLW | -DOOR LEAF WIDTH |
| DLH | -DOOR LEAF HEIGHT |
| COW | -CLEAR OPENING WIDTH |
| COH | -CLEAR OPENING HEIGHT |

[illegible]

PROJECT : TESTING PROJECT

CONTRACTOR : DNV

ANTI BLAST RESISTANT DOOR
PLAN, ELEVATION & DETAILS

DESIGNED BY:	SSW	DRAWING NUMBER	REV. NO.
CHECKED BY:	Enr. AZIZAH ARIFAH 28-07-2013		
APPROVED BY:	Enr. AZIZAH ARIFAH		
DRAWN BY:	SSW 28-07-2013		
SUBMITTED BY:			
SCALE: AS SHOWN		DN--01	01
DWG. REF. NO.			
		DWT 1 OF 1 DWG	

